

КАРТЫ ЗОН ОРШ

СХЕМА D

Децентрализованная структура: зонные ОРШ (сплиттеры 1:64)
при едином узле OLT · шесть сельских населённых пунктов ВКО
3 089 обслуживаемых домохозяйств · 36 зонных ОРШ + 6 ЦУ · ОРШ в центрах секторов, фидеры в границе НП

6

3 089

36 + 6

1 498,3 км

сельских населённых пунктов

домохозяйств (ДХ)


зонных ОРШ + ЦУ (OLT)

суммарного волокна

СОДЕРЖАНИЕ

№	Село	ДХ	Зон ОРШ + ЦУ	Волокно, км	Магистраль, км	Дроп, км	Стр.
01	Верхнеберезовка	1 029	14 + 1	524,8	33,6	41,7	2
02	Солнечное	124	0 + 1	90,0	5,3	5,2	3
03	Перевальное	376	4 + 1	218,5	11,6	15,8	4
04	Винное	622	9 + 1	329,9	21,4	27,2	5
05	Пригородное	288	3 + 1	141,2	9,0	13,0	6
06	Алтайский	650	6 + 1	193,9	9,6	24,0	7
Итого по схеме D		3 089	36 + 6	1 498,3	90,5	126,9	

Топология сетей, муфты и дропы соответствуют схемам A/B/C без изменений; меняется только размещение сплиттеров 1:64 (зонные ОРШ).
Подложка карт — спутниковые снимки Google z18: Верхнеберезовка — мозаика, остальные сёла — обрезанные кадры пользователя.
Полная ведомость материалов схемы D — в сводной таблице «Сводная_таблица_материалов_FTTH_ВКО_каскад.xlsx», лист «Схема D».
Печать: длинная сторона страниц соответствует А3 (420 мм); растр ~194 DPI.

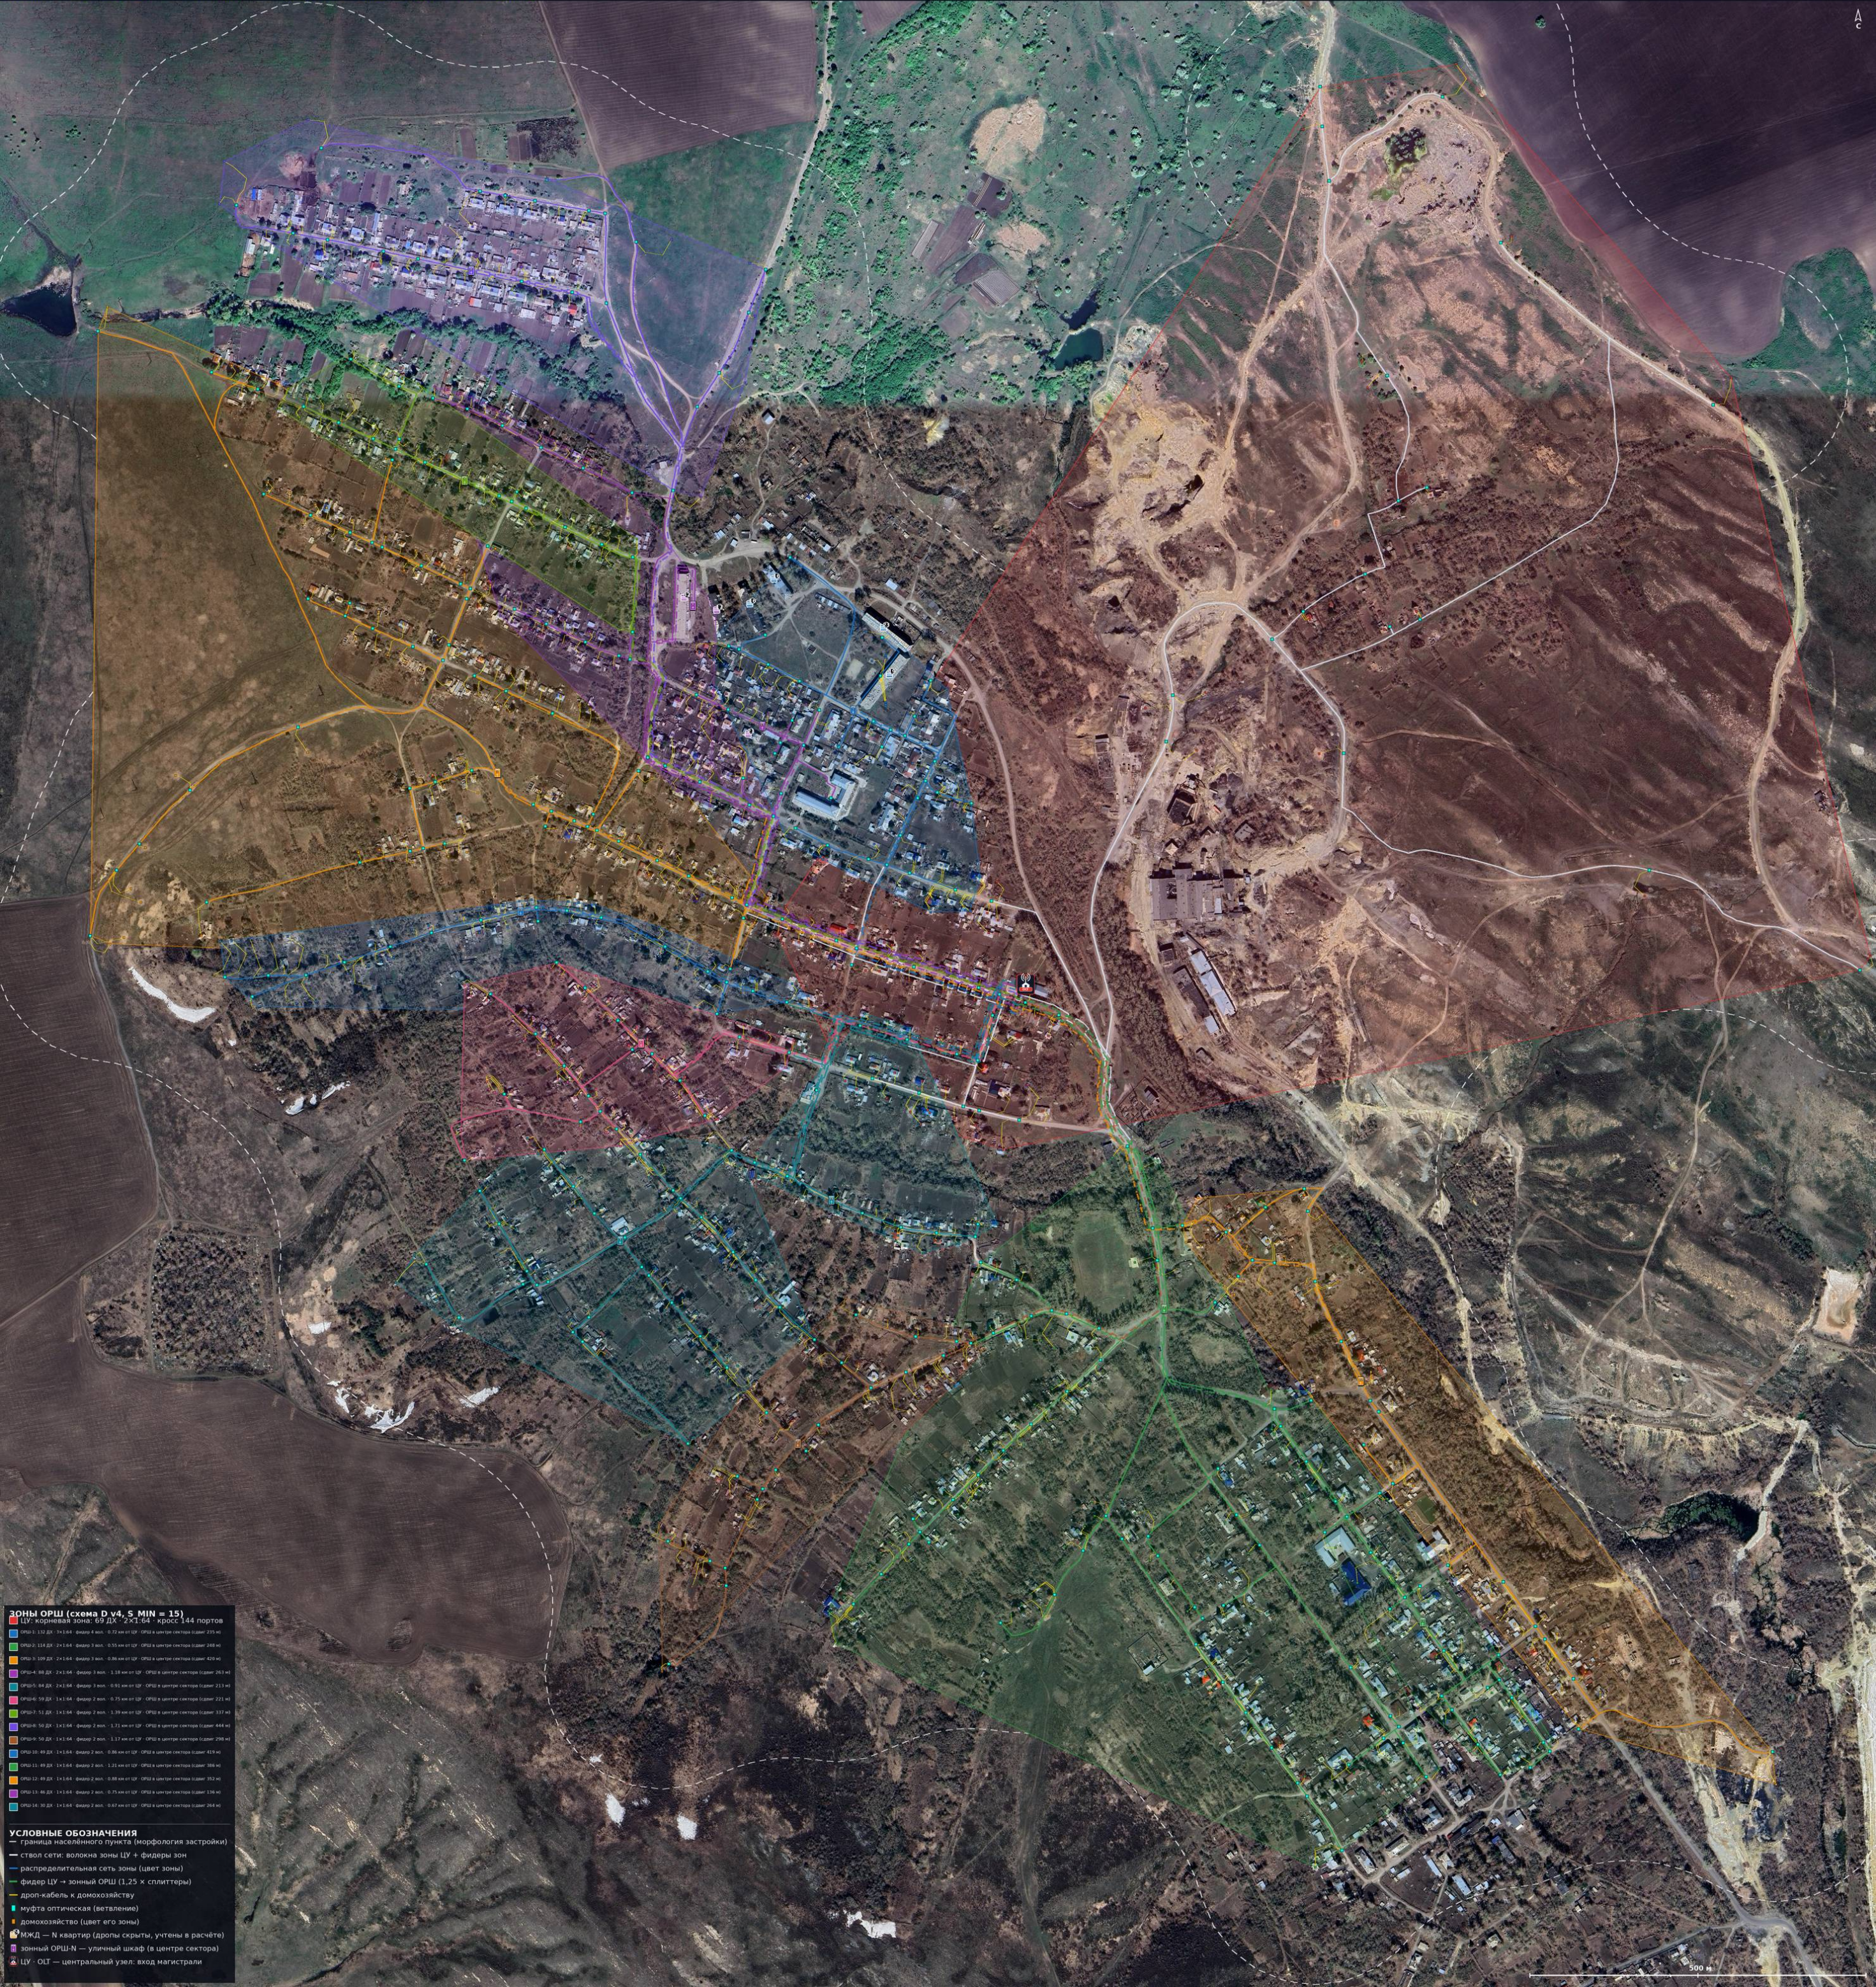

ДХ: 124 · зонных ОРШ: 0 + ЦУ · волокно-км: 90.0 · магистраль: 5.3 км · дроп-кабель: 5.2 км · сплиттеры 1×64: 2



ЗОНЫ ОРШ (схема D v4, S_MIN = 15)
■ ЦУ: корневая зона: 124 ДХ · 2×1:64 · кросс 144 портов
□ --: зонные ОРШ не образуются: село компактное, экономия ниже S_MIN

- УСЛОВНЫЕ ОБОЗНАЧЕНИЯ**
- граница населённого пункта (морфология застройки)
 - ствол сети: волокна зоны ЦУ + фидеры зон
 - распределительная сеть зоны (цвет зоны)
 - фидер ЦУ → зонный ОРШ (1,25 × сплиттеры)
 - дроп-кабель к домохозяйству
 - муфта оптическая (ветвление)
 - домохозяйство (цвет его зоны)
 - 🏠 МЖД — N квартир (дропа скрыты, учтены в расчёте)
 - 🏠 зонный ОРШ-N — уличный шкаф (в центре сектора)
 - 📶 ЦУ · OLT — центральный узел: вход магистрали

500 м

ЗОНЫ ОРШ (схема D v4, S MIN = 15)

■ ЦУ: корневая зона: 35 ДХ · 1x1:64 · кросс 144 портов

■ ОРШ-1: 156 ДХ · 3x1:64 · фидер 4 вол. · 0.29 км от ЦУ · ОРШ в центре сектора (сдвиг 143 м)

■ ОРШ-2: 69 ДХ · 2x1:64 · фидер 3 вол. · 1.39 км от ЦУ · ОРШ в центре сектора (сдвиг 346 м)

■ ОРШ-3: 60 ДХ · 1x1:64 · фидер 2 вол. · 0.56 км от ЦУ · ОРШ в центре сектора (сдвиг 254 м)

■ ОРШ-4: 56 ДХ · 1x1:64 · фидер 2 вол. · 0.81 км от ЦУ · ОРШ в центре сектора (сдвиг 155 м)

УСЛОВНЫЕ ОБОЗНАЧЕНИЯ

— граница населённого пункта (морфология застройки)

— ствол сети: волокна зоны ЦУ + фидеры зон

— распределительная сеть зоны (цвет зоны)

— фидер ЦУ → зонный ОРШ (1,25 x сплиттеры)

— дроп-кабель к домохозяйству


■ муфта оптическая (ветвление)

■ домохозяйство (цвет его зоны)

🏠 МЖД — N квартир (дропы скрыты, учтены в расчёте)

📦 зонный ОРШ-N — уличный шкаф (в центре сектора)

📶 ЦУ · OLT — центральный узел: вход магистрали

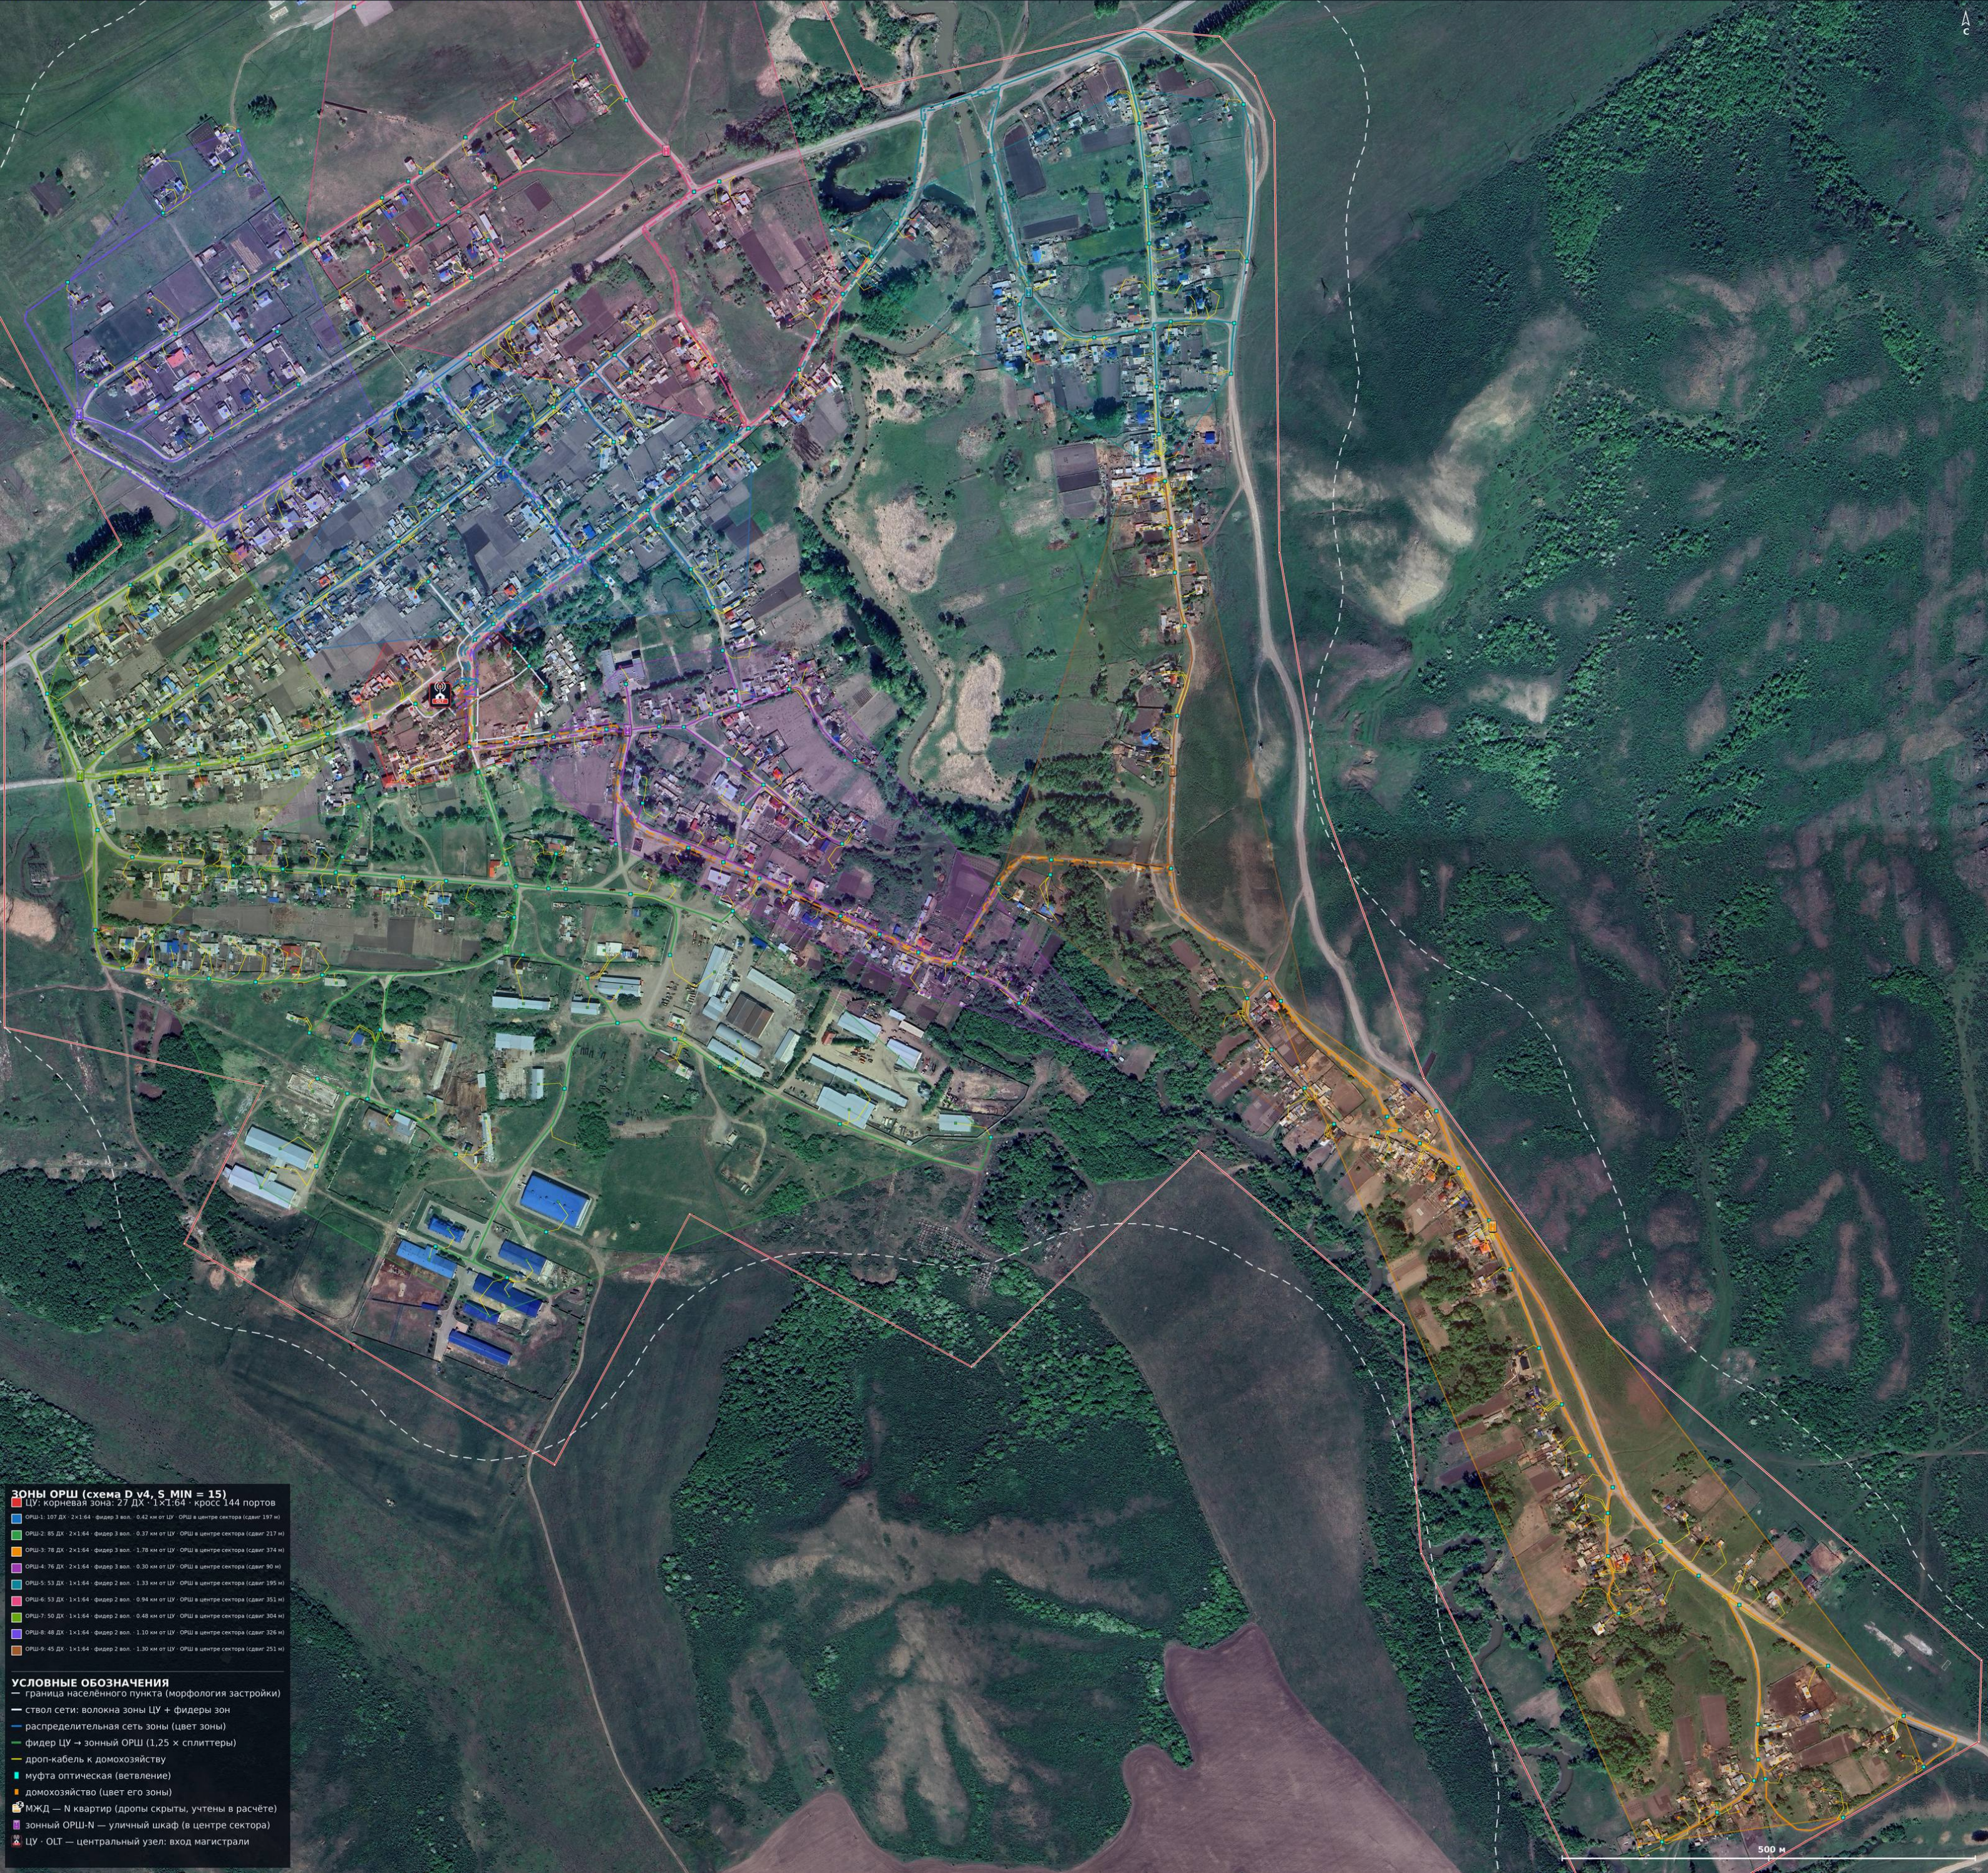

ЗОНЫ ОРШ (схема D v4, S MIN = 15)

- ЦУ: корневая зона: 27 ДХ · 1x1.64 · кросс 144 портов
- ОРШ-1: 107 ДХ · 2x1.64 · фидер 3 вол. · 0.42 км от ЦУ · ОРШ в центре сектора (сдвиг 197 м)
- ОРШ-2: 85 ДХ · 2x1.64 · фидер 3 вол. · 0.37 км от ЦУ · ОРШ в центре сектора (сдвиг 217 м)
- ОРШ-3: 78 ДХ · 2x1.64 · фидер 3 вол. · 1.78 км от ЦУ · ОРШ в центре сектора (сдвиг 374 м)
- ОРШ-4: 76 ДХ · 2x1.64 · фидер 3 вол. · 0.30 км от ЦУ · ОРШ в центре сектора (сдвиг 90 м)
- ОРШ-5: 53 ДХ · 1x1.64 · фидер 2 вол. · 1.33 км от ЦУ · ОРШ в центре сектора (сдвиг 195 м)
- ОРШ-6: 53 ДХ · 1x1.64 · фидер 2 вол. · 0.94 км от ЦУ · ОРШ в центре сектора (сдвиг 351 м)
- ОРШ-7: 50 ДХ · 1x1.64 · фидер 2 вол. · 0.48 км от ЦУ · ОРШ в центре сектора (сдвиг 304 м)
- ОРШ-8: 48 ДХ · 1x1.64 · фидер 2 вол. · 1.10 км от ЦУ · ОРШ в центре сектора (сдвиг 326 м)
- ОРШ-9: 45 ДХ · 1x1.64 · фидер 2 вол. · 1.30 км от ЦУ · ОРШ в центре сектора (сдвиг 251 м)


УСЛОВНЫЕ ОБОЗНАЧЕНИЯ

- граница населённого пункта (морфология застройки)
- ствол сети: волокна зоны ЦУ + фидеры зон
- распределительная сеть зоны (цвет зоны)
- фидер ЦУ → зонный ОРШ (1,25 x сплиттеры)
- дроп-кабель к домохозяйству
- муфта оптическая (ветвление)
- домохозяйство (цвет его зоны)
- МЖД — N квартир (дропы скрыты, учтены в расчёте)
- зонный ОРШ-N — уличный шкаф (в центре сектора)
- ЦУ · OLT — центральный узел: вход магистрали

с. Пригородное — схема D (v4): зонные ОРШ в центрах секторов, фидеры — кратчайшие пути в границе НП

г. Риддер · — · кадр пользователя (0.19 м/рх, спутник Google z18 ×2) · МЖД — один значок с числом квартир, дропы квартир не прорисованы (в расчёте); граница НП — морфология застройки (шаг 46)

ДХ: 288 · зонных ОРШ: 3 + ЦУ · волокно-км: 141.2 · магистраль: 9.0 км · дроп-кабель: 13.0 км · сплиттеры 1×64: 6

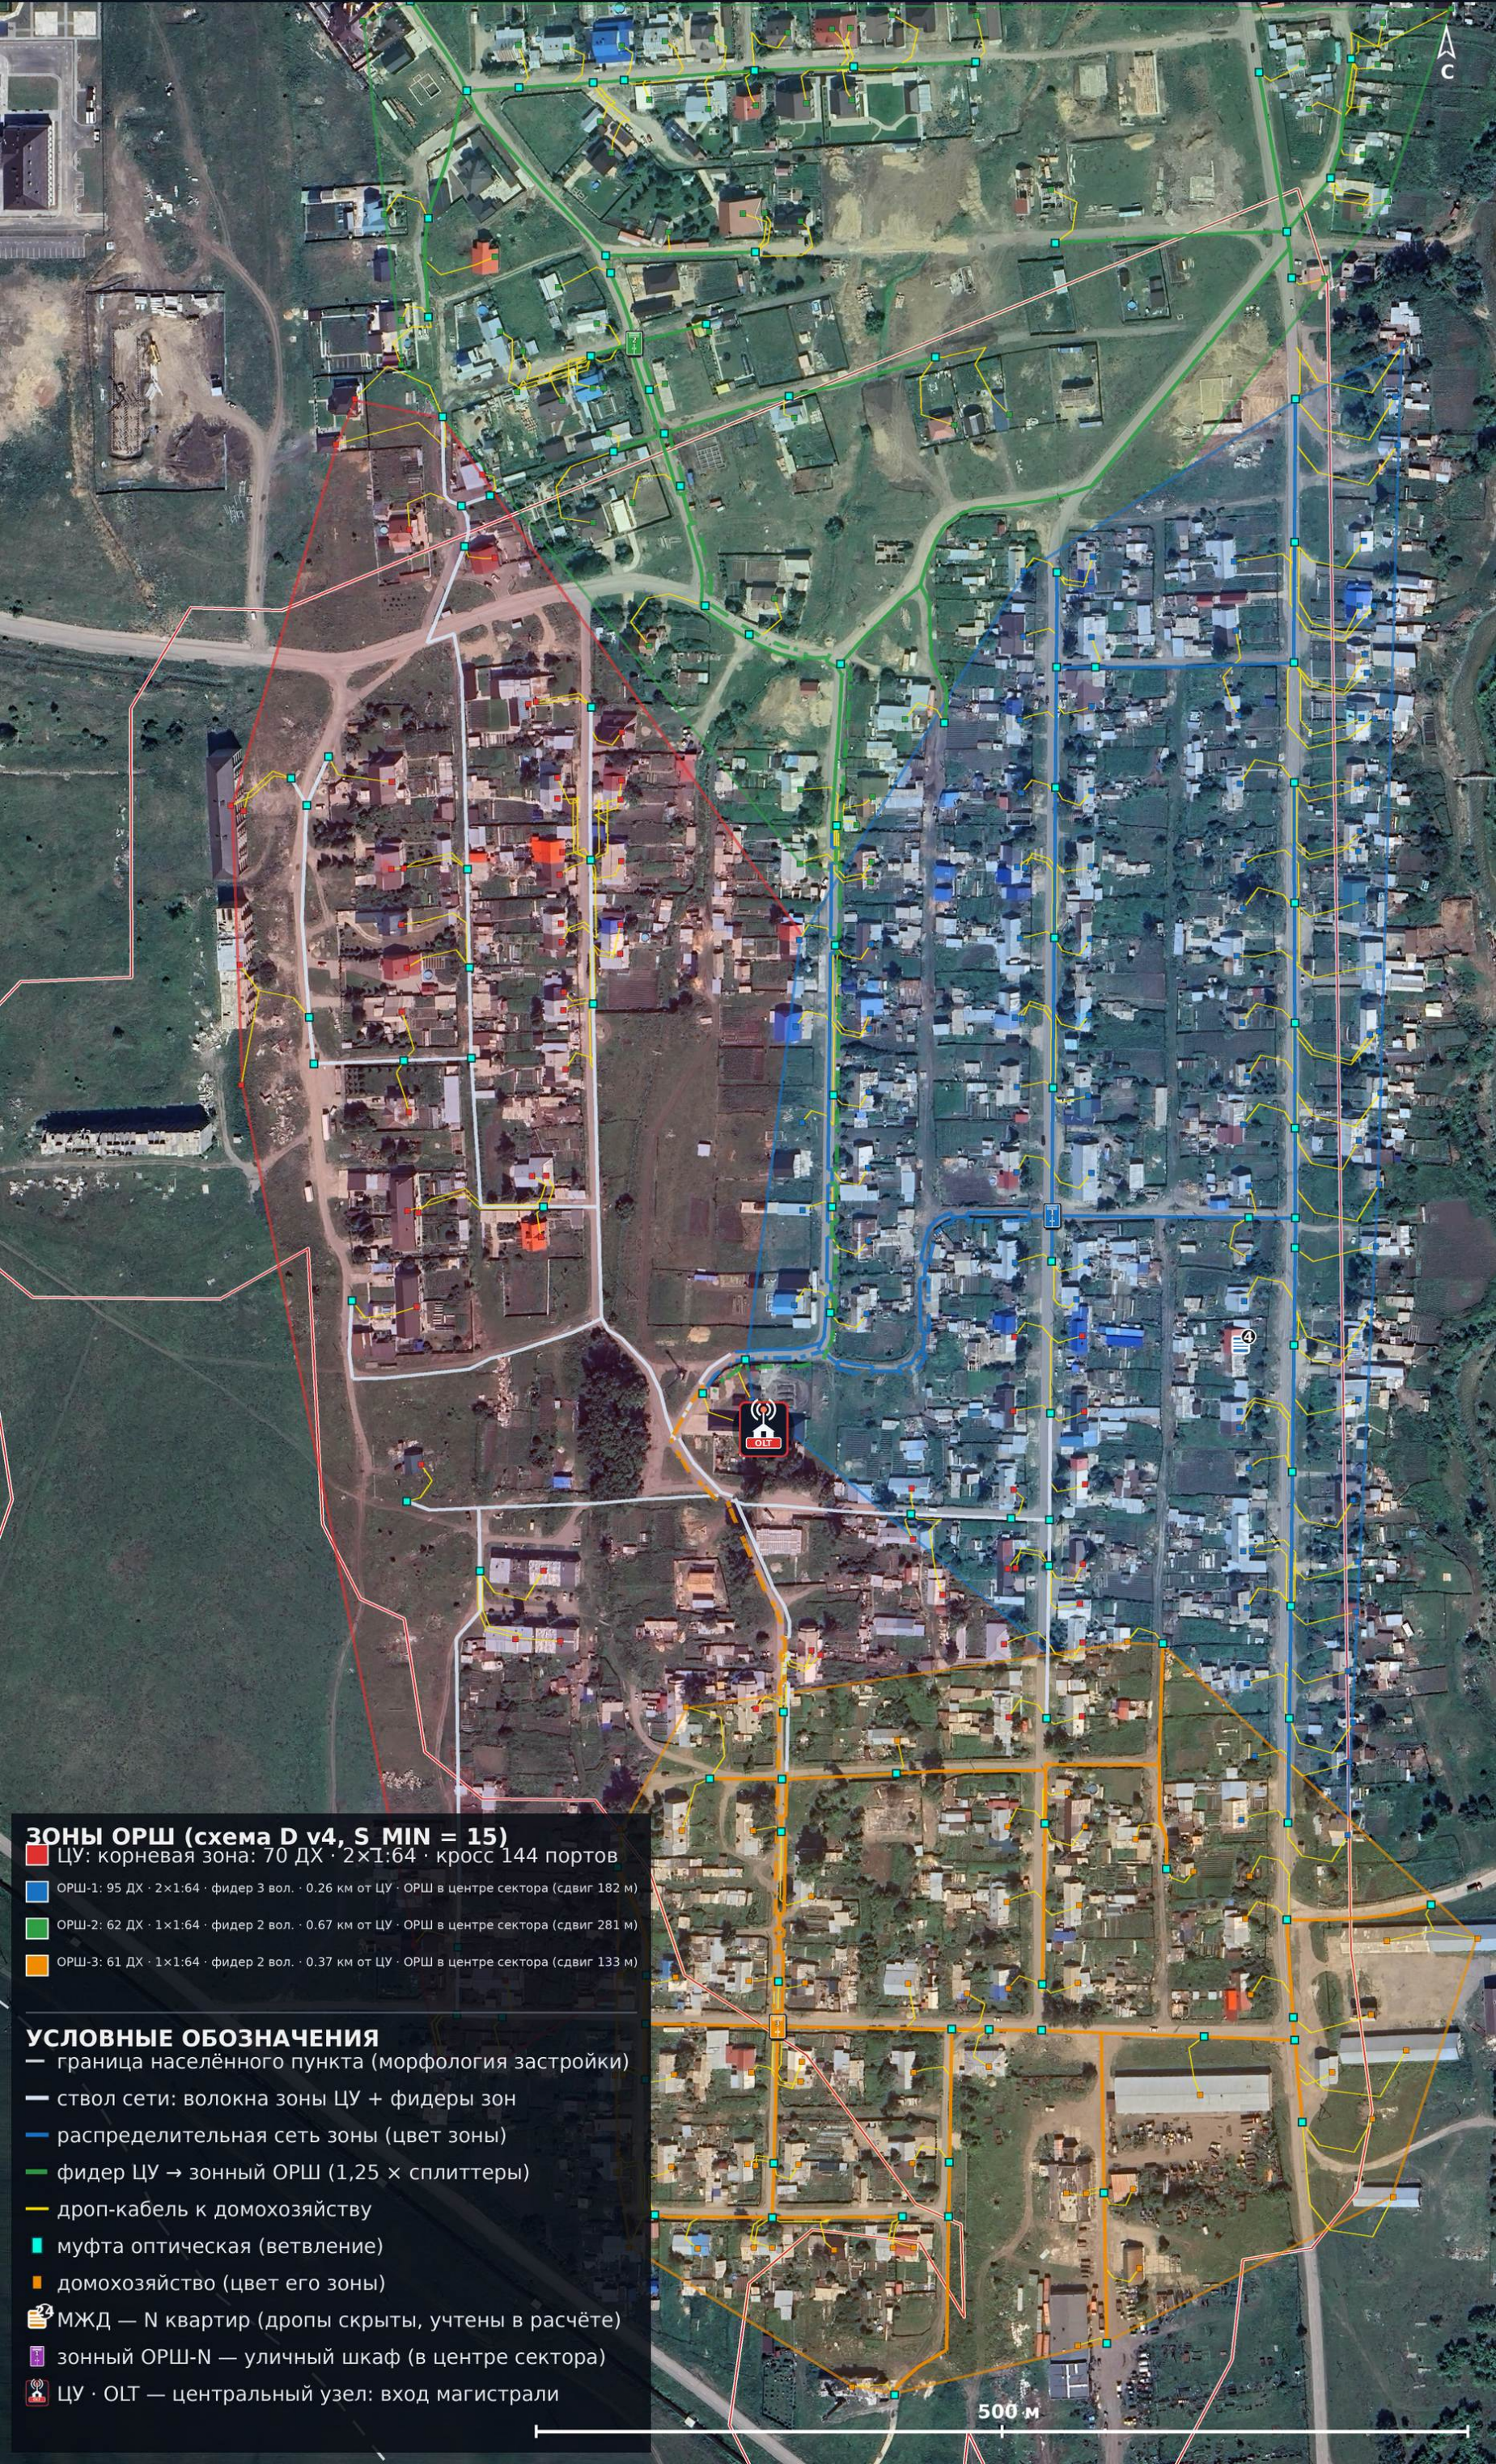

ЗОНЫ ОРШ (схема D v4, S MIN = 15)

ЦУ: корневая зона: 70 ДХ · 2×1:64 · кросс 144 портов

ОРШ-1: 95 ДХ · 2×1:64 · фидер 3 вол. · 0.26 км от ЦУ · ОРШ в центре сектора (сдвиг 182 м)

ОРШ-2: 62 ДХ · 1×1:64 · фидер 2 вол. · 0.67 км от ЦУ · ОРШ в центре сектора (сдвиг 281 м)

ОРШ-3: 61 ДХ · 1×1:64 · фидер 2 вол. · 0.37 км от ЦУ · ОРШ в центре сектора (сдвиг 133 м)

УСЛОВНЫЕ ОБОЗНАЧЕНИЯ

граница населённого пункта (морфология застройки)

ствол сети: волокна зоны ЦУ + фидеры зон

распределительная сеть зоны (цвет зоны)

фидер ЦУ → зонный ОРШ (1,25 × сплиттеры)

дроп-кабель к домохозяйству

муфта оптическая (ветвление)


домохозяйство (цвет его зоны)

МЖД — N квартир (дропы скрыты, учтены в расчёте)

зонный ОРШ-N — уличный шкаф (в центре сектора)

ЦУ · OLT — центральный узел: вход магистрали

500 м

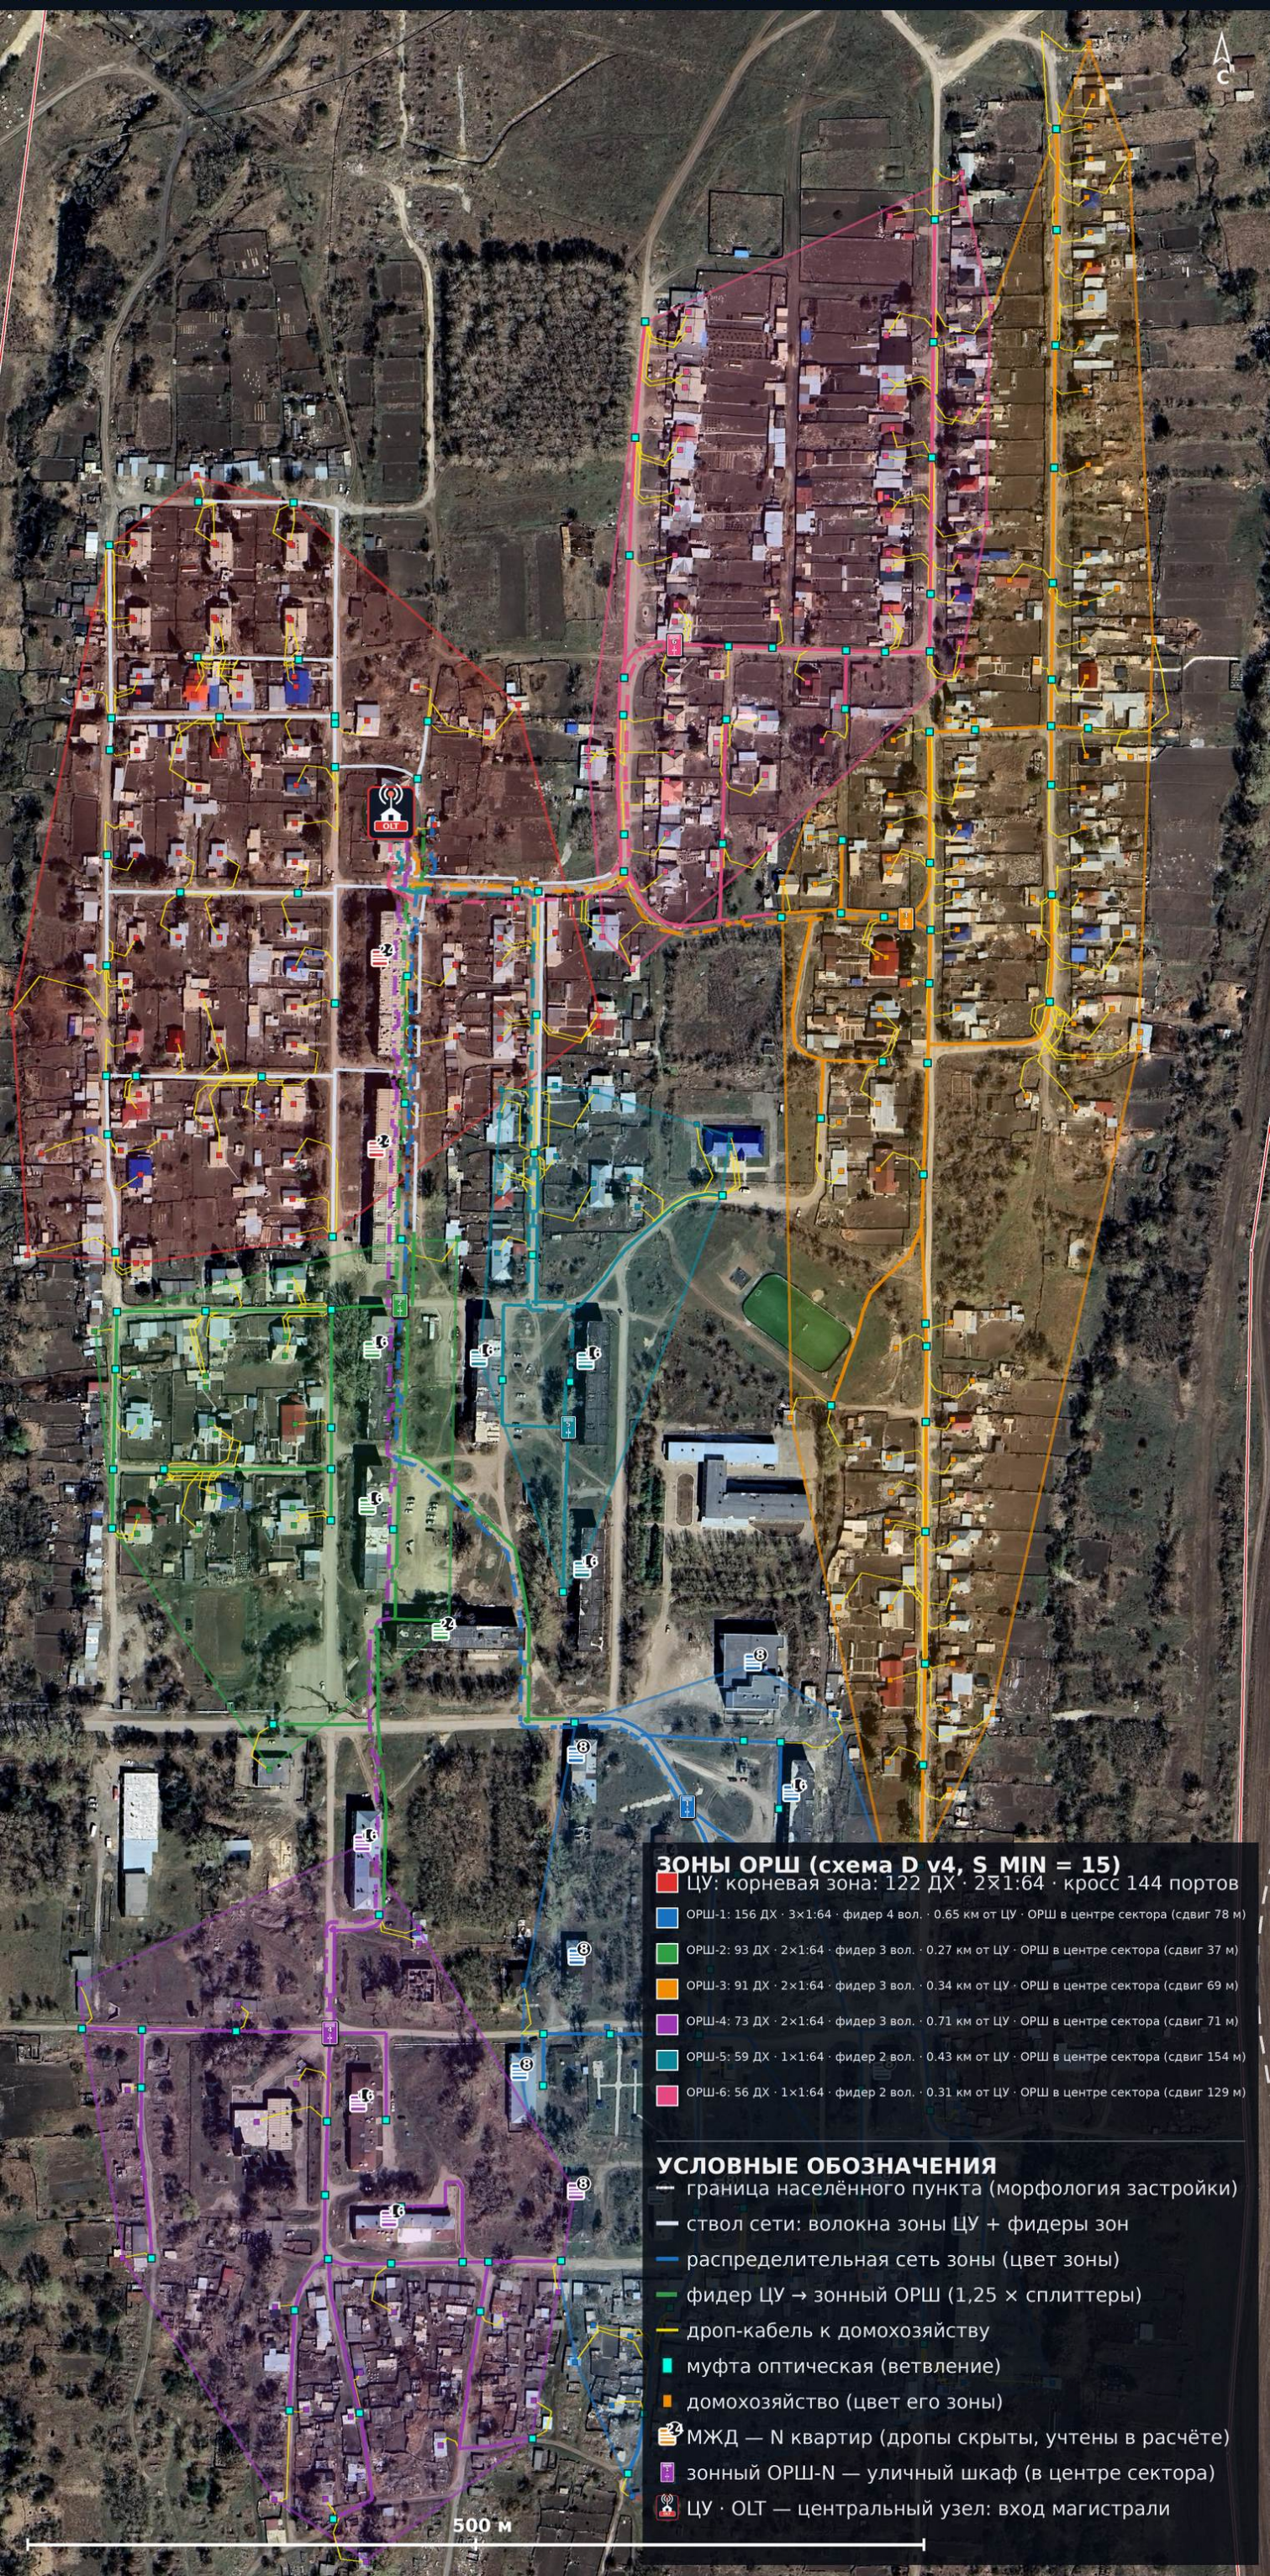

ЗОНЫ ОРШ (схема D v4, S MIN = 15)

- ЦУ: корневая зона: 122 ДХ · 2×1:64 · кросс 144 портов
- ОРШ-1: 156 ДХ · 3×1:64 · фидер 4 вол. · 0.65 км от ЦУ · ОРШ в центре сектора (сдвиг 78 м)
- ОРШ-2: 93 ДХ · 2×1:64 · фидер 3 вол. · 0.27 км от ЦУ · ОРШ в центре сектора (сдвиг 37 м)
- ОРШ-3: 91 ДХ · 2×1:64 · фидер 3 вол. · 0.34 км от ЦУ · ОРШ в центре сектора (сдвиг 69 м)
- ОРШ-4: 73 ДХ · 2×1:64 · фидер 3 вол. · 0.71 км от ЦУ · ОРШ в центре сектора (сдвиг 71 м)
- ОРШ-5: 59 ДХ · 1×1:64 · фидер 2 вол. · 0.43 км от ЦУ · ОРШ в центре сектора (сдвиг 154 м)
- ОРШ-6: 56 ДХ · 1×1:64 · фидер 2 вол. · 0.31 км от ЦУ · ОРШ в центре сектора (сдвиг 129 м)

УСЛОВНЫЕ ОБОЗНАЧЕНИЯ

- граница населённого пункта (морфология застройки)
- ствол сети: волокна зоны ЦУ + фидеры зон
- распределительная сеть зоны (цвет зоны)
- фидер ЦУ → зонный ОРШ (1,25 x сплиттеры)
- дроп-кабель к домохозяйству
- муфта оптическая (ветвление)
- домохозяйство (цвет его зоны)
- МЖД — N квартир (дропа скрыты, учтены в расчёте)
- зонный ОРШ-N — уличный шкаф (в центре сектора)
- ЦУ · OLT — центральный узел: вход магистрали